

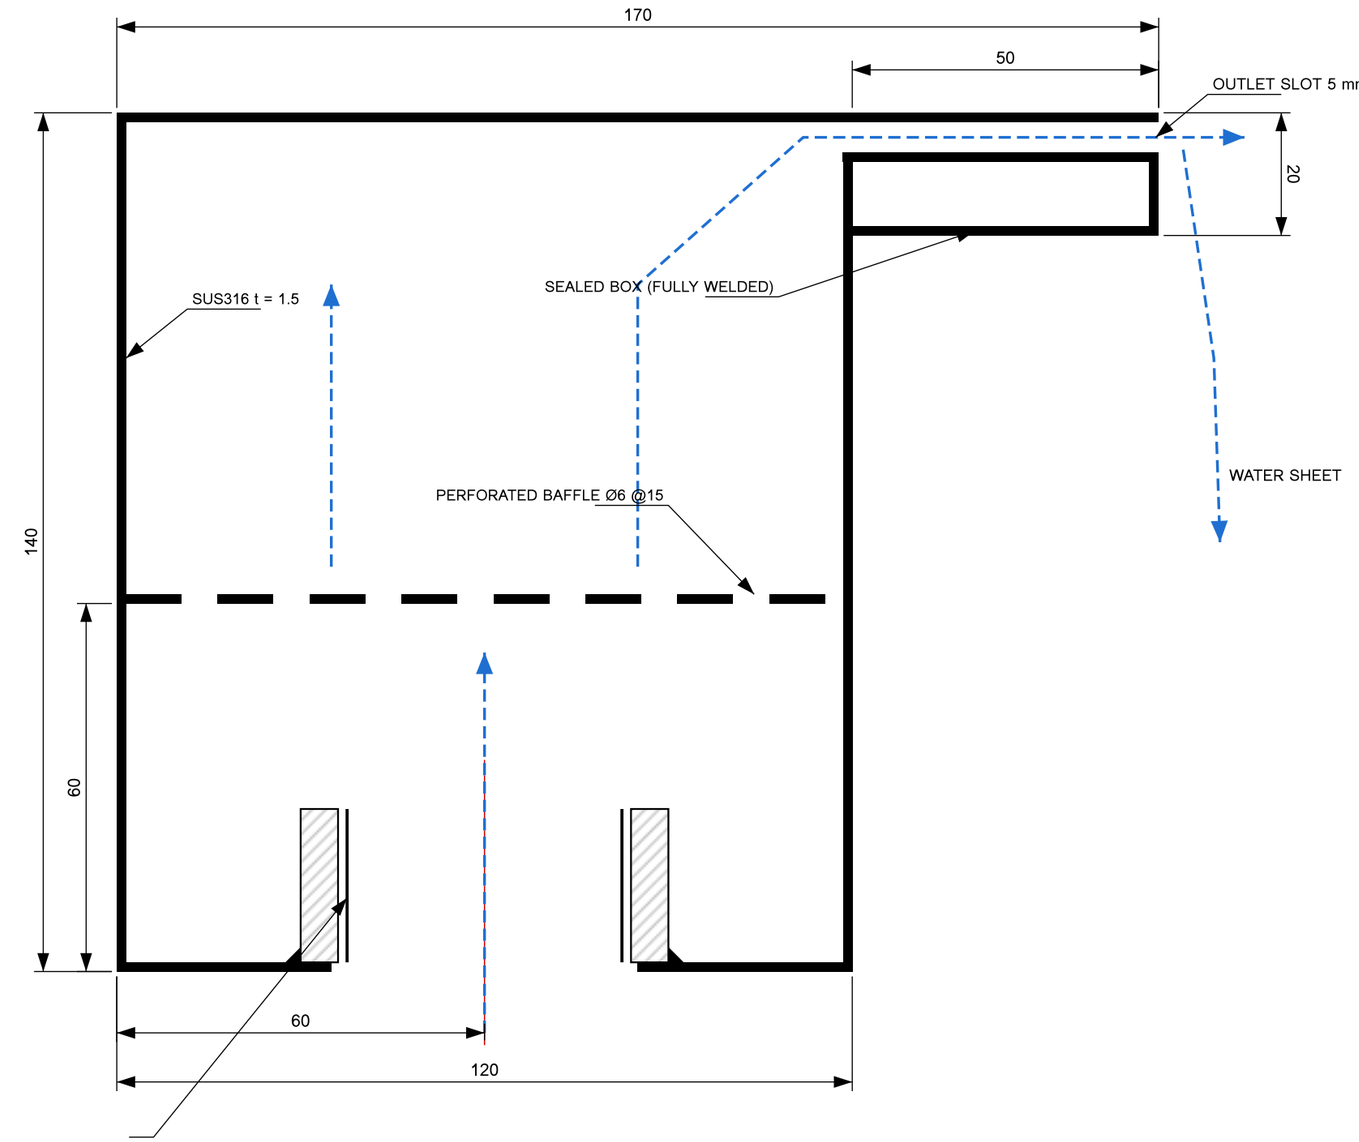


FEMALE THREAD G1½" (BSPP)
SUS316 SOCKET Ø60 × 25 H


SECTION A-A
SCALE 1:1

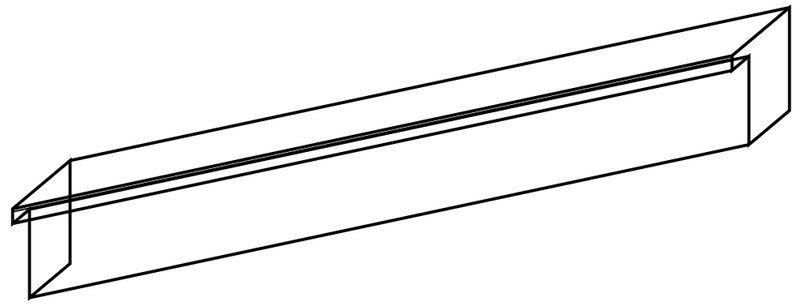

ISOMETRIC VIEW (NOT TO SCALE)

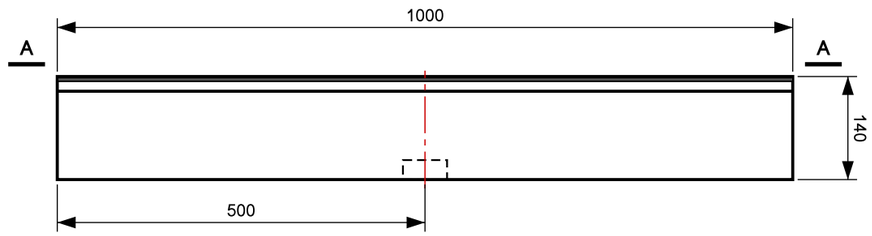

FRONT VIEW (OUTLET SIDE)

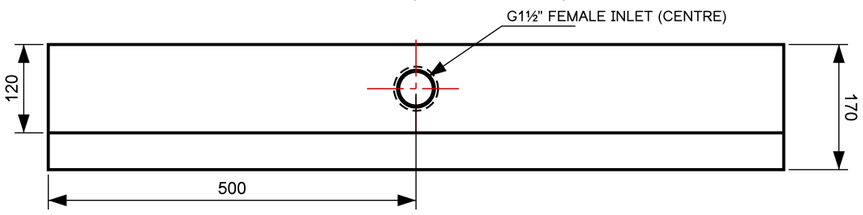

BOTTOM VIEW

WONDER TECHNOLOGY CO., LTD.	
PROJECT: VELRA THONGLOR	
STAINLESS STEEL 316 WATER CURTAIN L 1000 × 170 × 140 mm • INLET G1½" FEMALE THREAD	
MATERIAL: SUS316 t = 1.5 mm	DRAWING No.: WC-316-1000-01
SCALE: AS SHOWN (A3)	UNITS: MILLIMETRES (mm)
QTY: 1 SET	DATE: 16/10/2026
DRAWN BY:	CHECKED / APPROVED: .....